

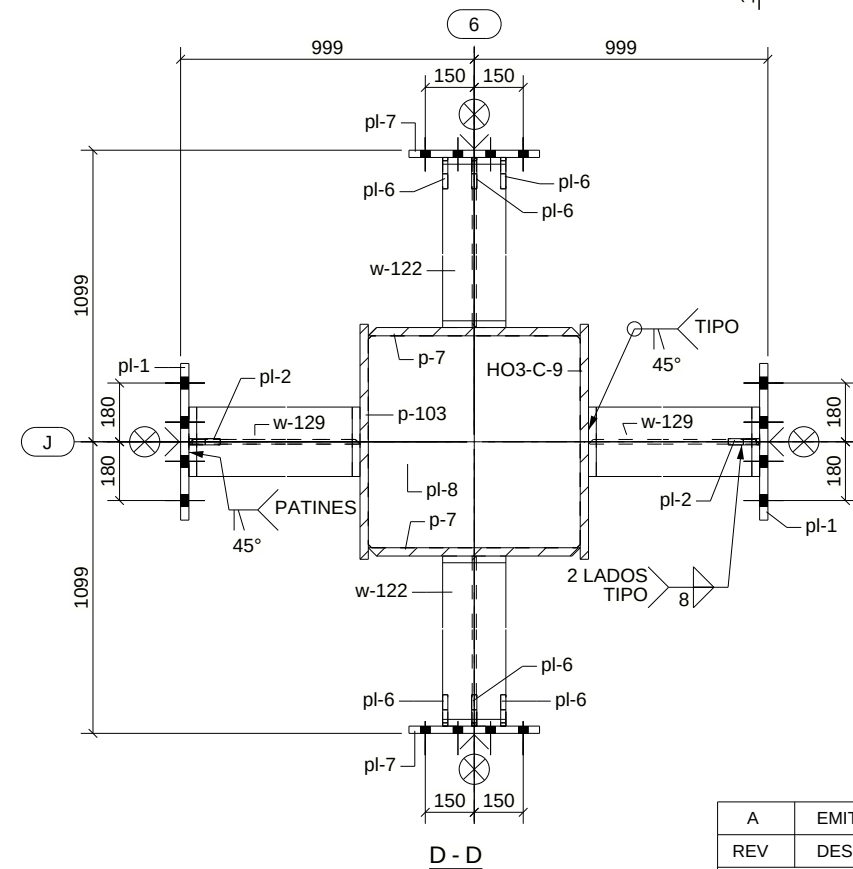
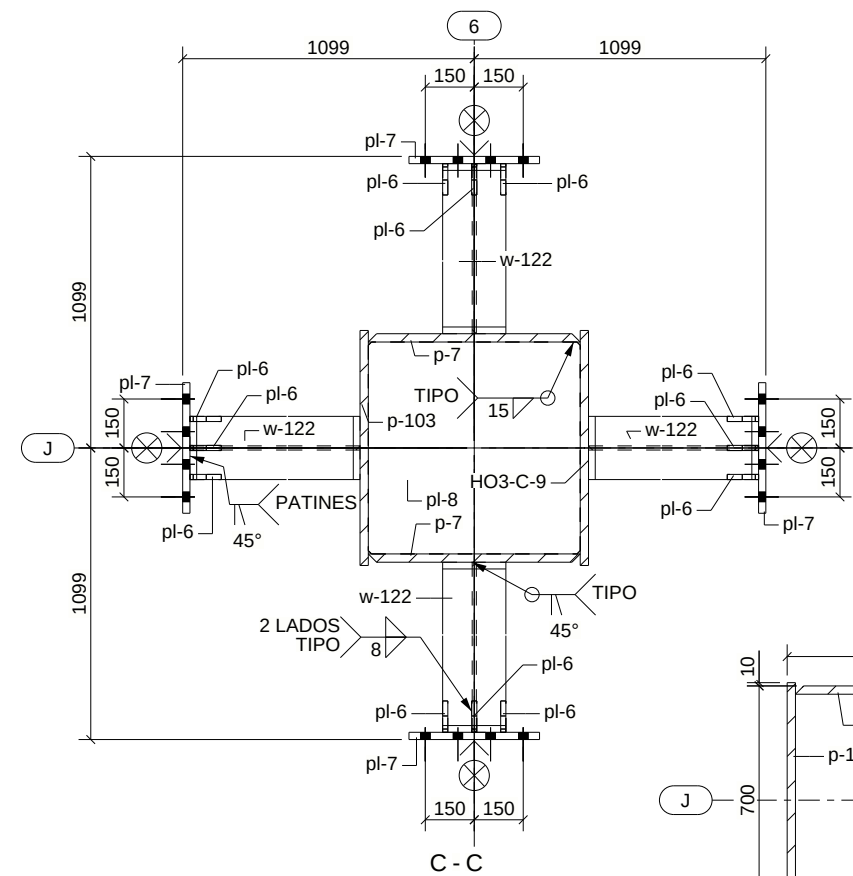
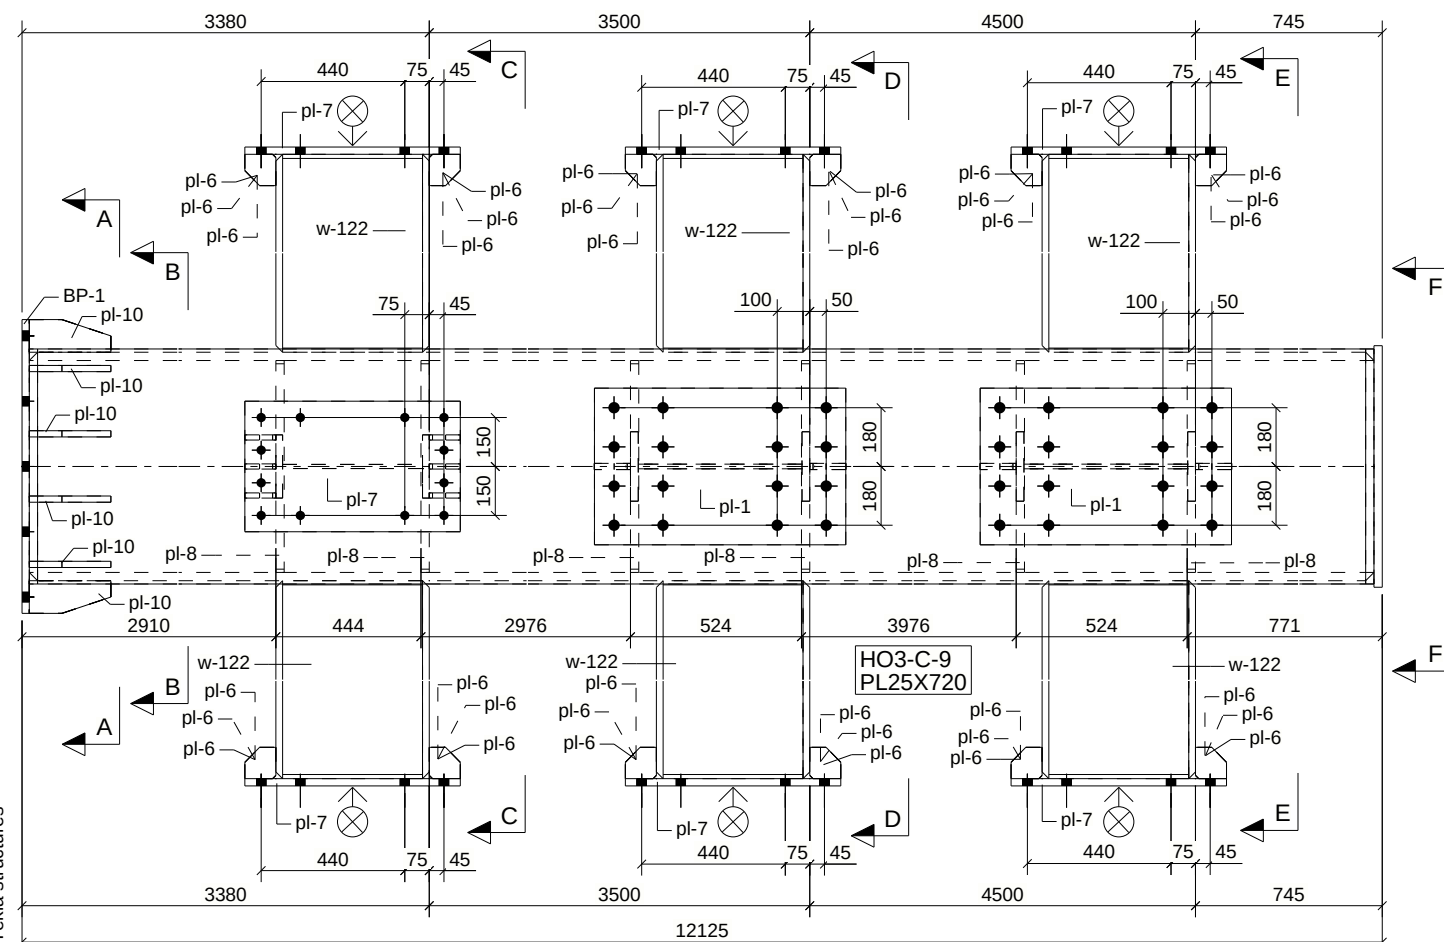
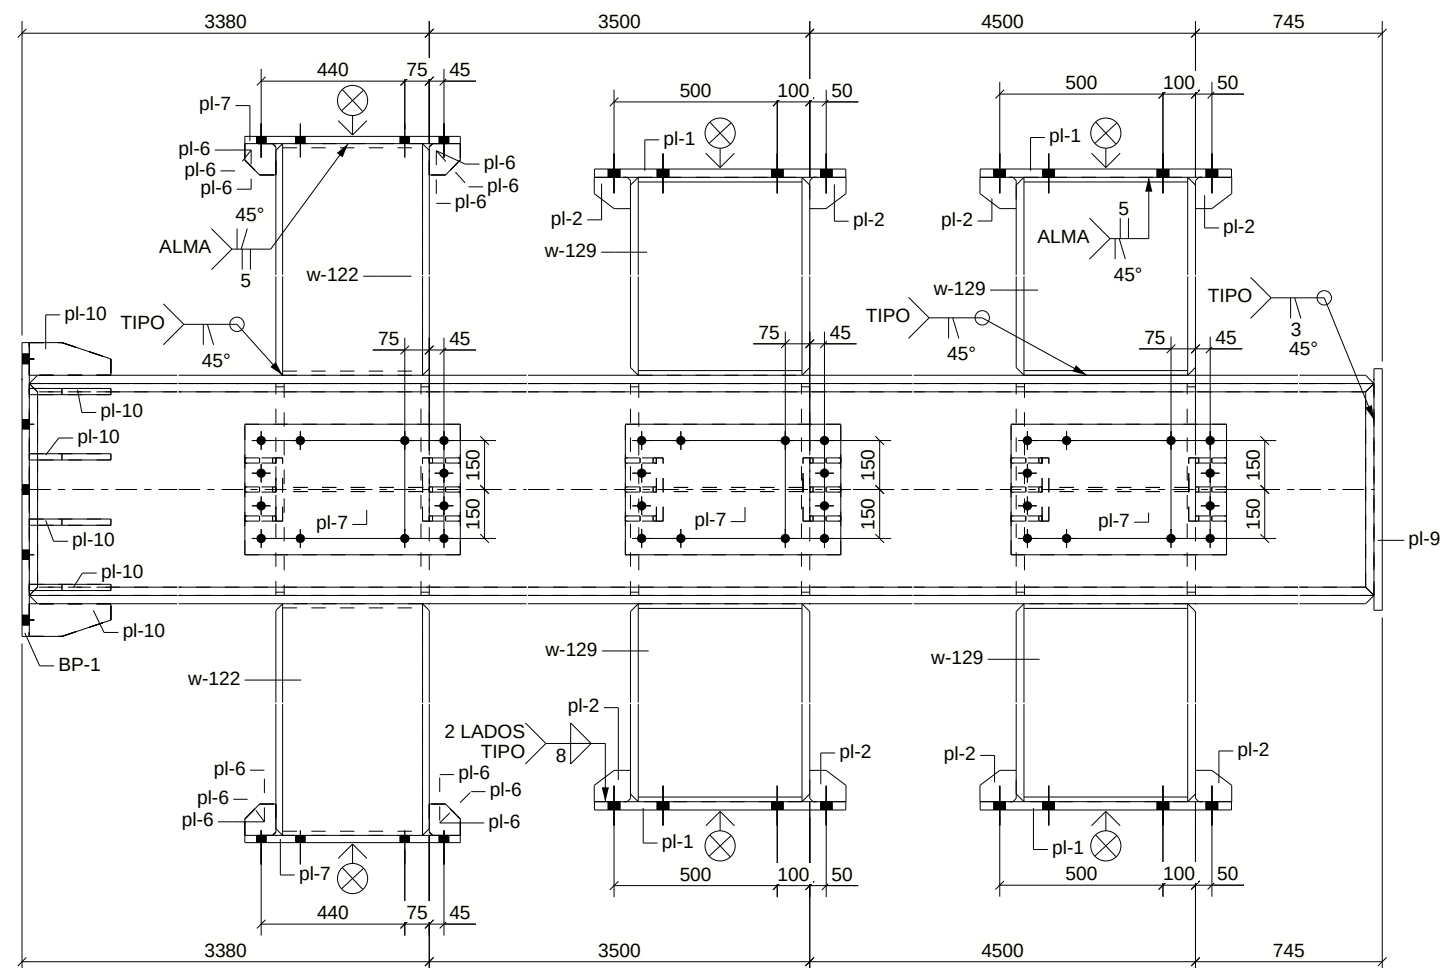
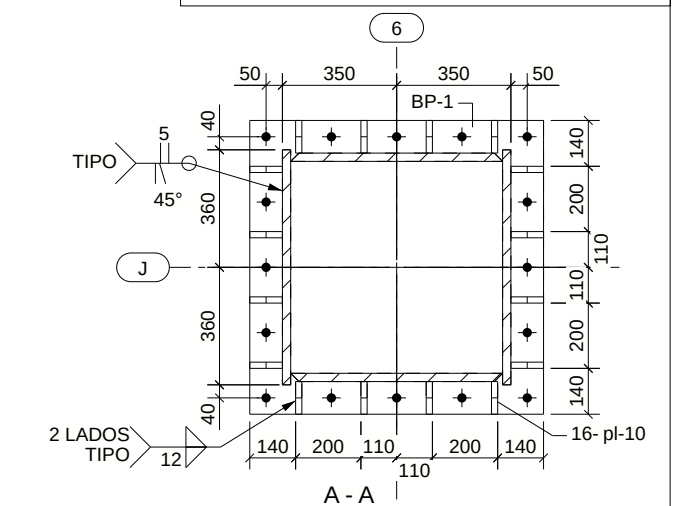


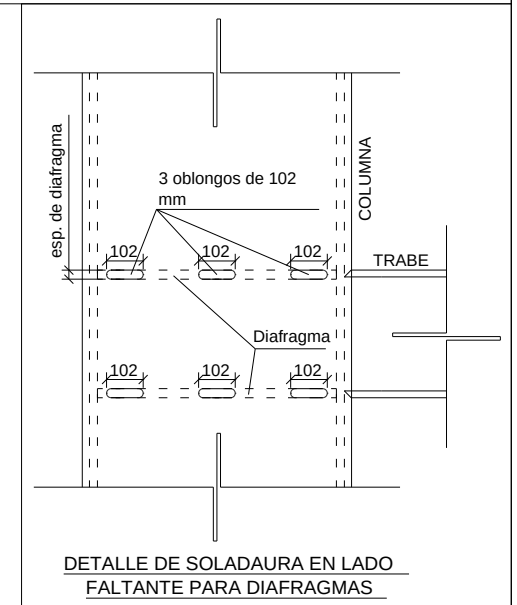

NOTAS GENERALES:

1. TODAS LAS SOLDADURAS SE APEGAN A LO ESPECIFICADO EN LA AWS D1.1
2. PARA TOLERANCIAS DIMENSIONALES SEGUIR AISC SPECIFICATION M2 Y AISC CODE OF STANDARD

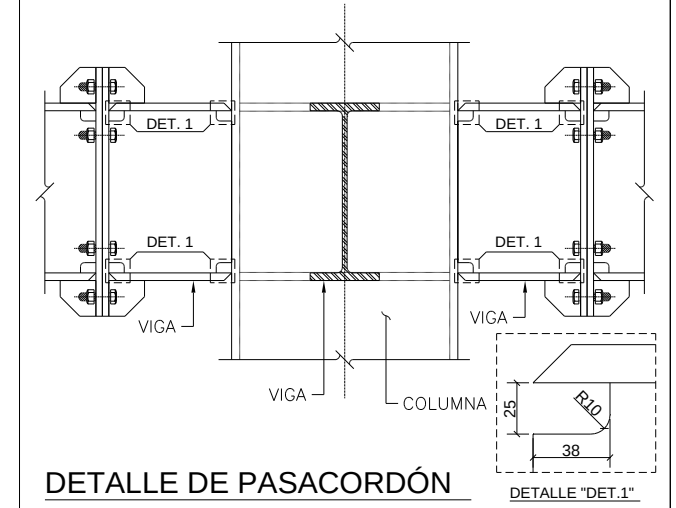

A	EMITIDO PARA APROBACIÓN Y/O COMENTARIOS	UAM	16/08/23
REV	DESCRIPCION	POR	FECHA
			EDITO:
			NOTAS:
PROYECTO	HOSPITAL GENERAL IMSS	CONTRATO:	No. DE PLANO:
CLIENTE			HO3-C-9 H1